


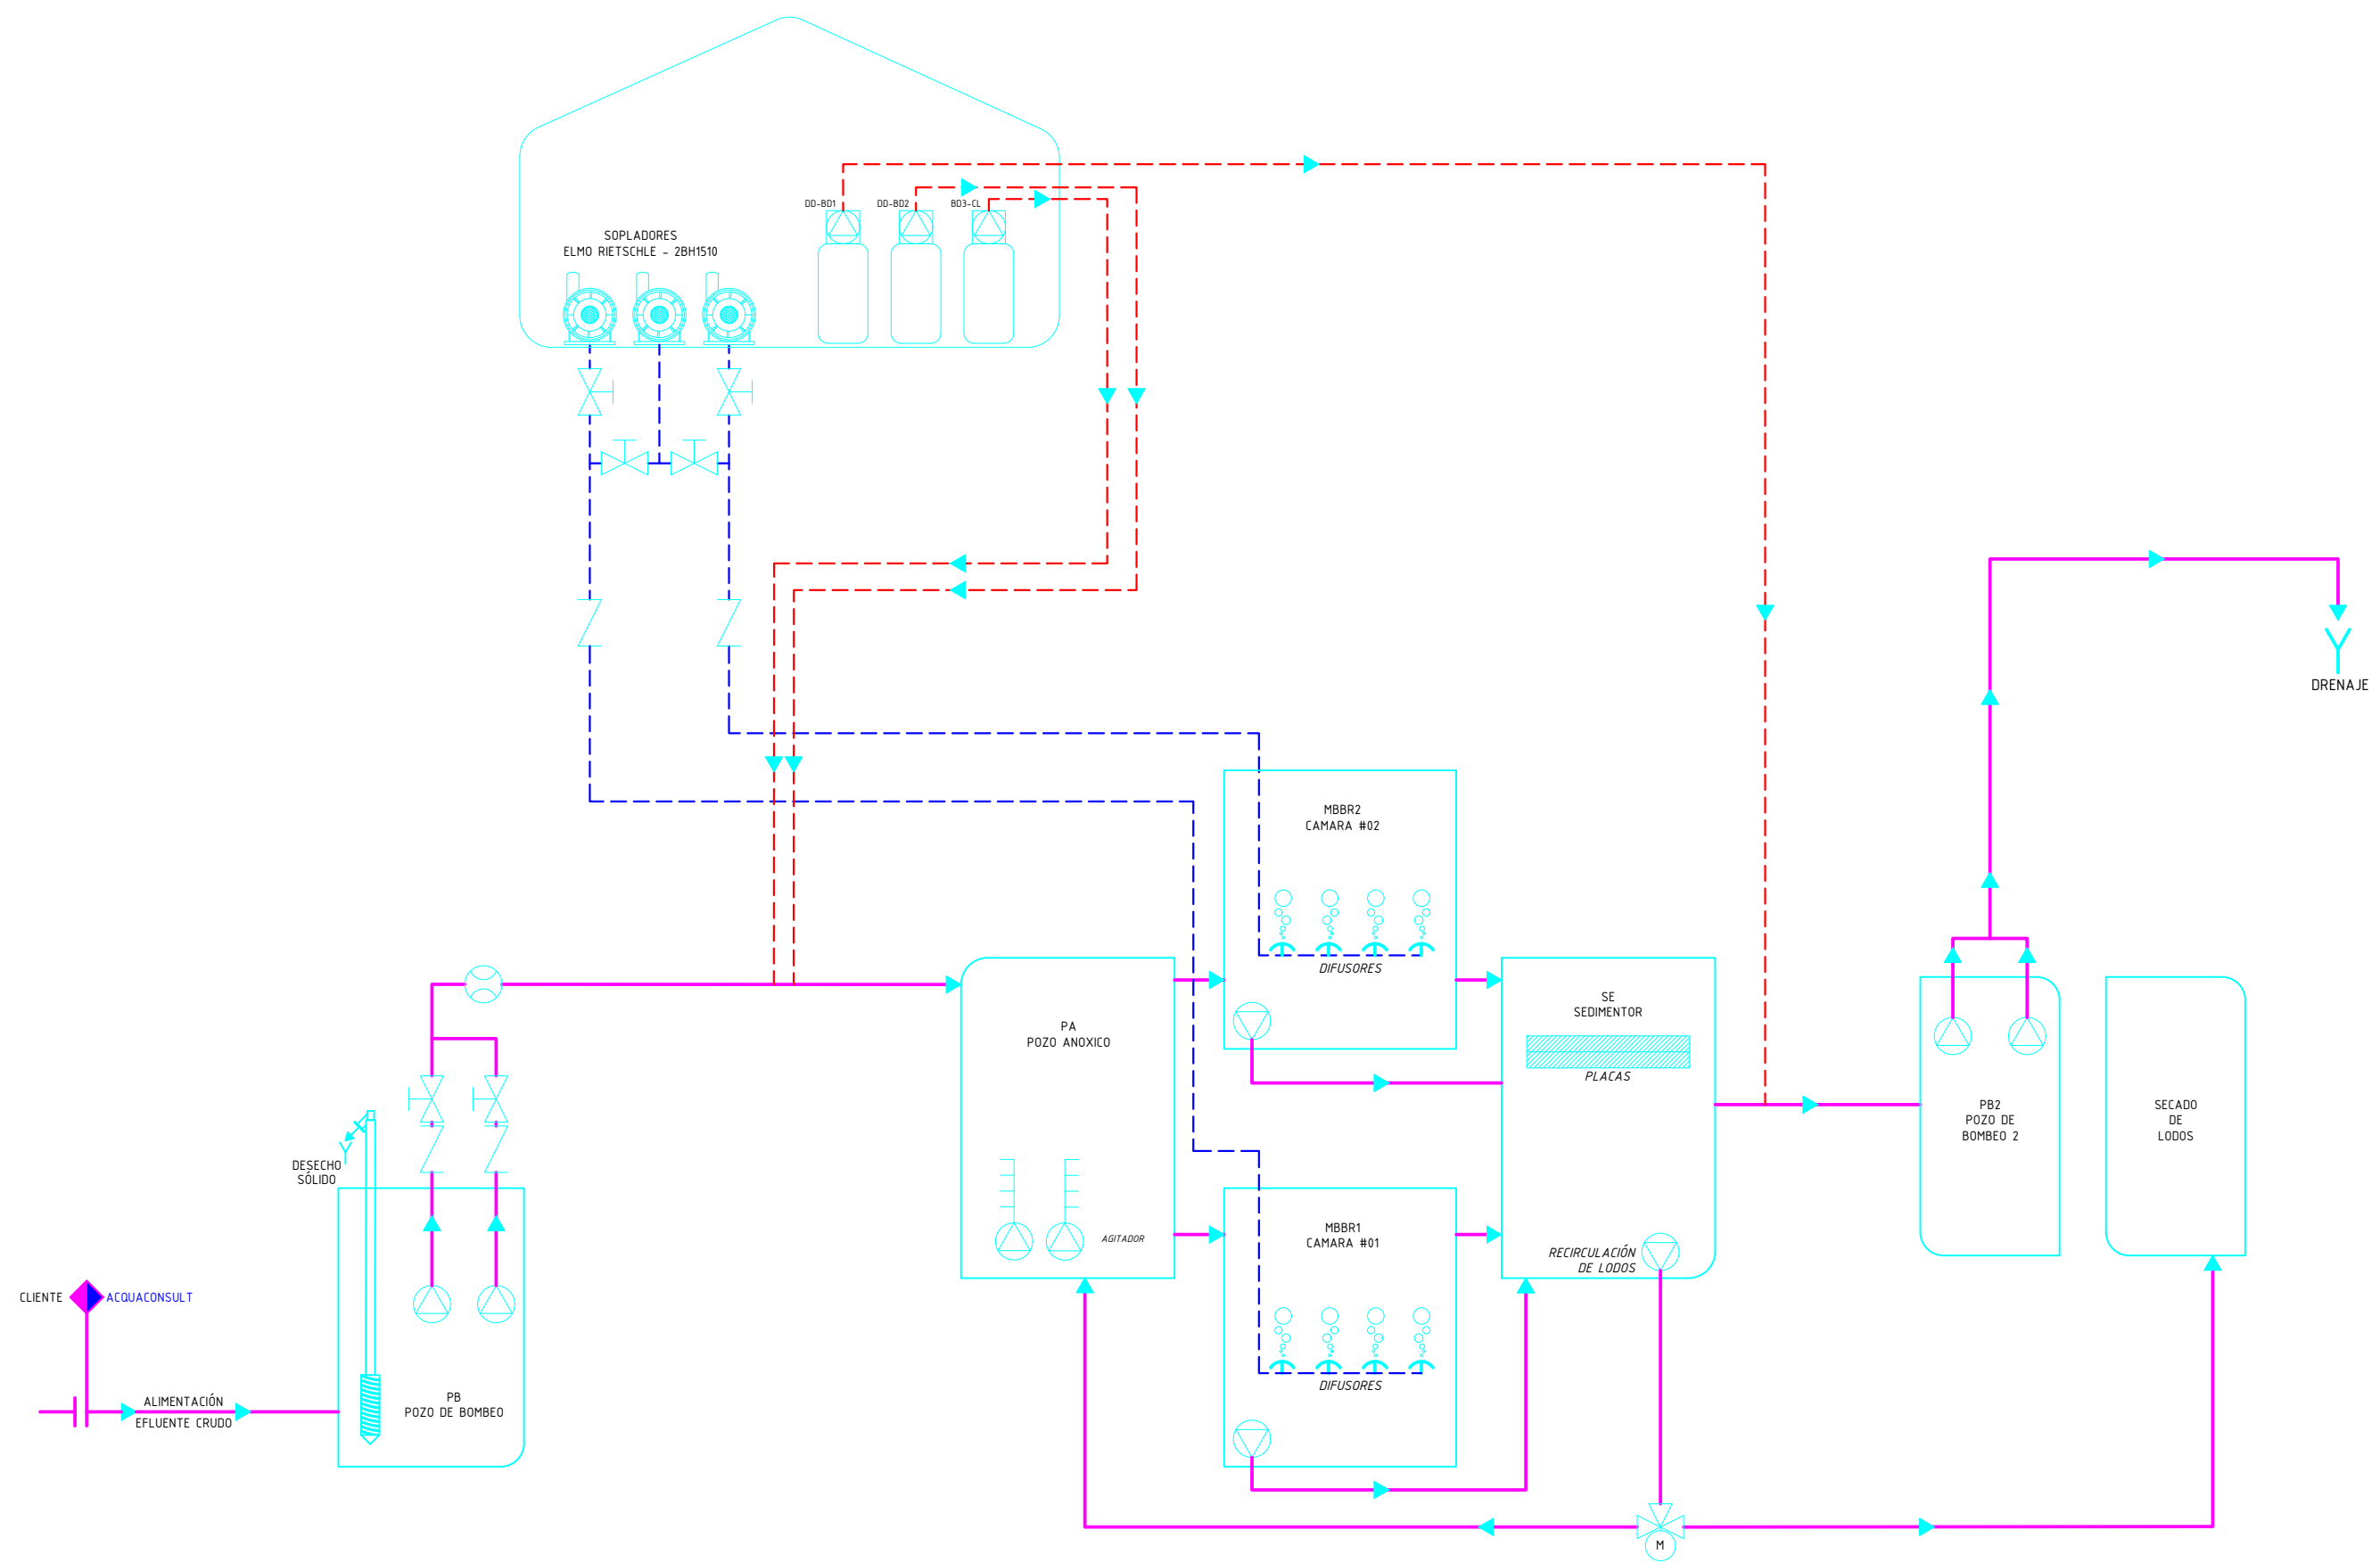

- REFERENCIAS**
- LINEA DE PROCESO.
 - AIRE A BAJA PRESION.
 - DOSIF. PRODUCTOS QUIMICOS.

AC6 AcquaConsult®		CLIENTE: SALUM & WENZ		PROYECTO: PTE-PARQUE INDUSTRIAL TAIWAN		
	FECHA	NOMBRE	FIRMA	TÍTULO: P&ID - FLUJOGRAMA		
DISEÑO	06/02/2026	EH				
REVISÓ	06/02/2026	JD		PLANO N°.: ...		REV. N°.: 0
APROBÓ	06/02/2026	RD		OT N°.: ...		ESC.: HOJA N°.: 0