


LISTA DE EQUIPOS		
REF.	DESCRIPCIÓN	CHECK
LSL-PBE	BAJO NIVEL POZO DE BOMBEO DE ENTRADA	
LSH-PBE	ALTO NIVEL DE POZO DE BOMBEO DE ENTRADA	
LSHH-PBE	MUY ALTO NIVEL POZO DE BOMBEO DE ENTRADA	
LSL-PBS	BAJO NIVEL POZO DE BOMBEO DE SALIDA	
LSH-PBS	ALTO NIVEL DE POZO DE BOMBEO DE SALIDA	
LSHH-PBS	MUY ALTO NIVEL POZO DE BOMBEO DE SALIDA	
B1-PBE	BOMBA 1 - POZO DE BOMBEO DE ENTRADA	
B2-PBE	BOMBA 2 - POZO DE BOMBEO DE ENTRADA	
BD1-PBE	BOMBA DOSIFICADORA 1 - POZO DE BOMBEO DE ENTRADA	
BD2-PBE	BOMBA DOSIFICADORA 2 - POZO DE BOMBEO DE ENTRADA	
BD3-CL	BOMBA DOSIFICADORA - CLORACIÓN	
AG1-RA	AGITADOR 1 - POZO ANOXICO (BOMBA SUMERGIBLE)	
AG1-RA	AGITADOR 2 - POZO ANOXICO (BOMBA SUMERGIBLE)	
SO1-BR1	SOPLADOR 1 - CAMARA 1 MBBR	
SO2-BR2	SOPLADOR 2 - CAMARA 2 MBBR	
SO3-BR1/2	SOPLADOR 3 - CAMARA 1/2 MBBR	
BL-BR1	BOMBA DE LODOS - CAMARA 1 MBBR	
BL-BR2	BOMBA DE LODOS - CAMARA 2 MBBR	
BL-SE	BOMBA DE LODOS - SEDIMENTADOR	
ZV-SE	VÁLVULA ACTUADA DE RECIRCULACIÓN DE LOFOS - SEDIMENTADOR	
B1-PBS	BOMBA DE ALIMENTACIÓN 1 - POZO DE BOMBEO 2	
B2-PBS	BOMBA DE ALIMENTACIÓN 2 - POZO DE BOMBEO 2	
VM	VALVULA MANUAL TIPO MARIPOSA	
VR	VALVULA DE RETENCION TIPO A CLAPETA	
FT-ENT	CAUDALIMETRO DE EFLUENTE DE ENTRADA	
TV-PBE	TAMIZ VERTICAL 1 - POZO DE BOMBEO	

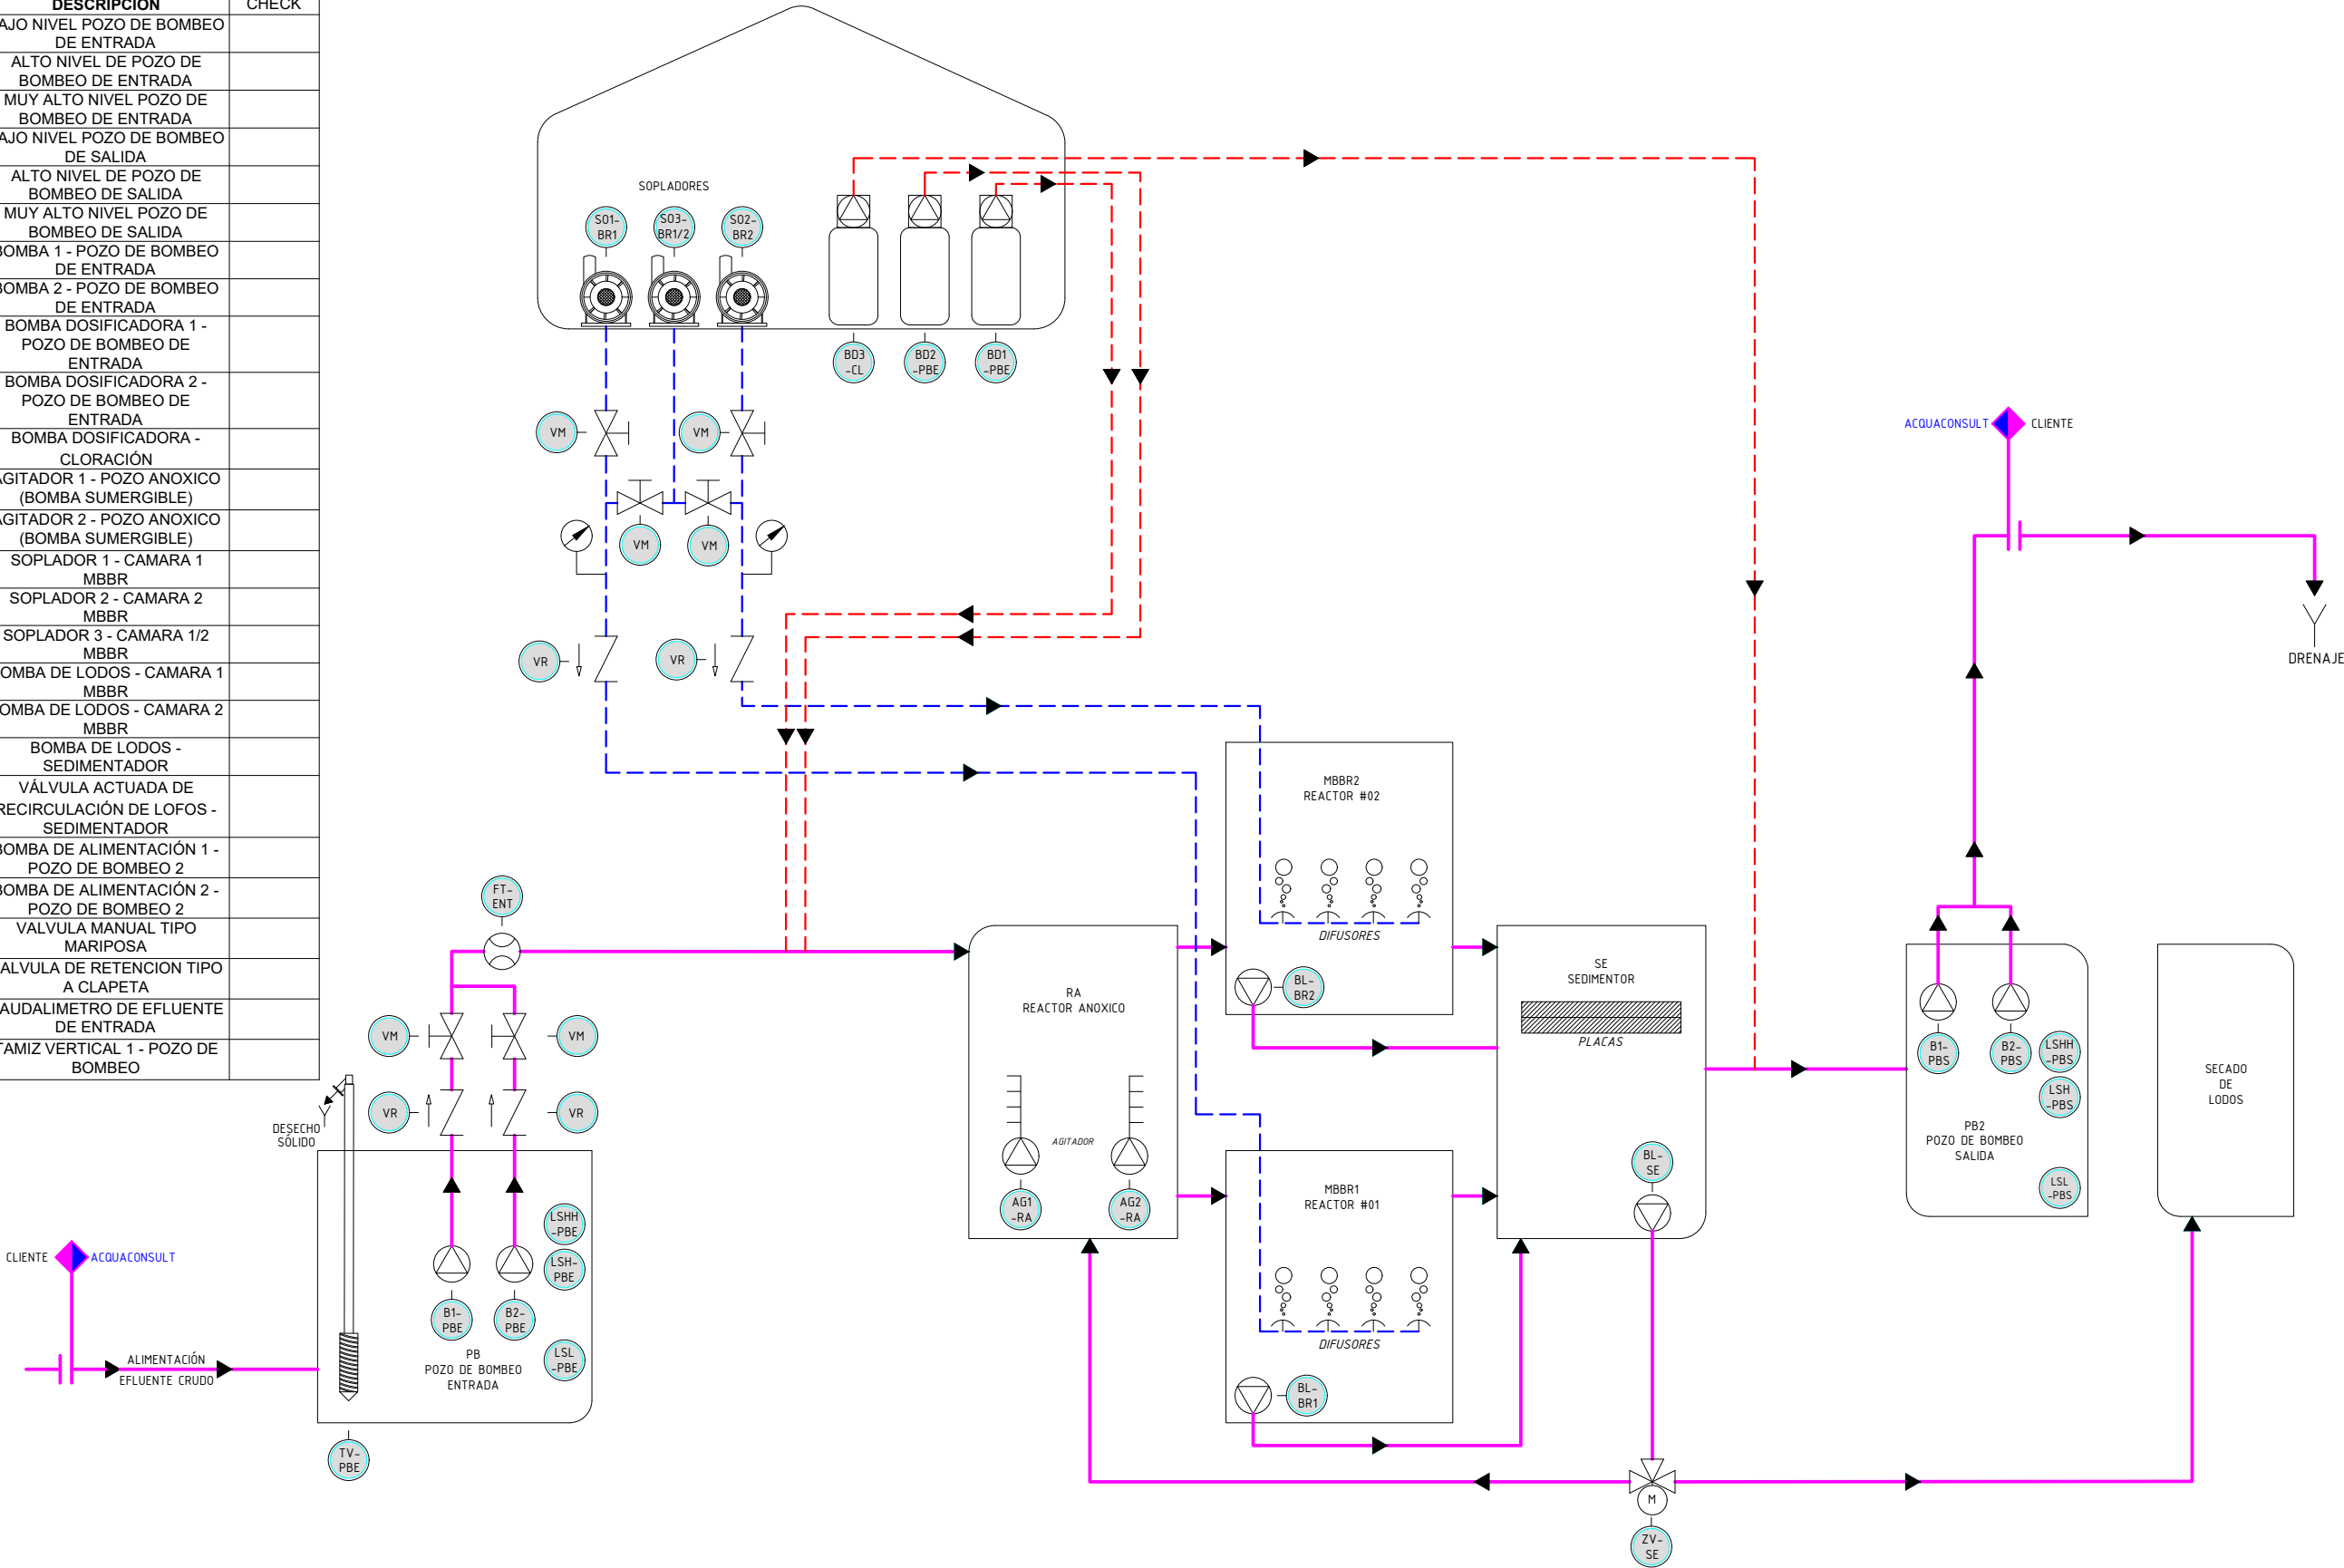

REFERENCIAS
— LINEA DE PROCESO.
- - - AIRE A BAJA PRESION.
- - - DOSIF. PRODUCTOS QUIMICOS.

AC6 AcquaConsult®		CLIENTE: SALUM & WENZ		PROYECTO: PTE-PARQUE INDUSTRIAL TAIWAN	
	FECHA	NOMBRE	FIRMA	TÍTULO: P&ID - FLUJOGRAMA	
DISEÑO	06/02/2026	EH			
REVISÓ	06/02/2026	JD			
APROBÓ	06/02/2026	RD			
				PLANO N°.: ...	REV. N°.: 0
				OT N°.: ...	HOJA N°.: 0
				ESC.: ...	